
Material:

Barra de Acero Inoxidable de AISI 316 Longitud: 1135 mm

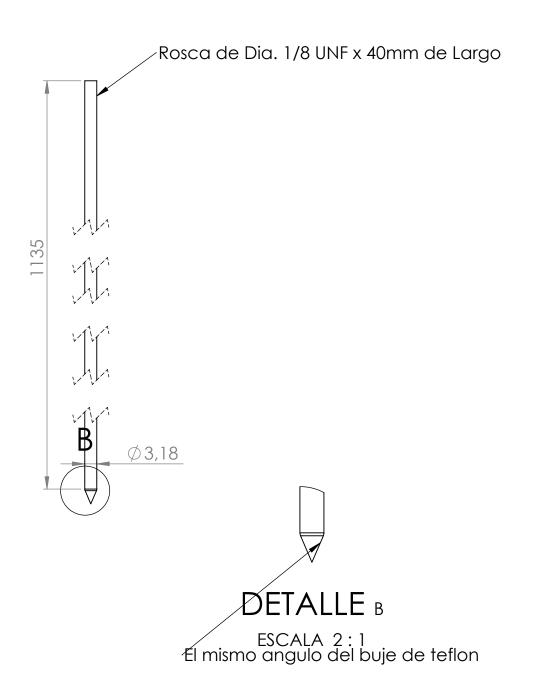

LAS CO	:					REBARBAR Y ROMPER ARISTAS VIVAS	NO CAMBIE LA ESCALA	REVISIÓN	
	NOMBRE	FIRMA		FECHA				τίτυιο:	
DIBUJ.									
VERIF.									
APROB.									
FABR.									
CALID.					MATERIAL	.:	N.º DE DIBINO	N.º DE DIBINO	<del>-</del> <del>-</del> ^ 1
							Varilla de la pipeta <sup>A4</sup>		
									. 1- 1
					PESO:			ESCALA:1:10	HOJA 1 DE 1